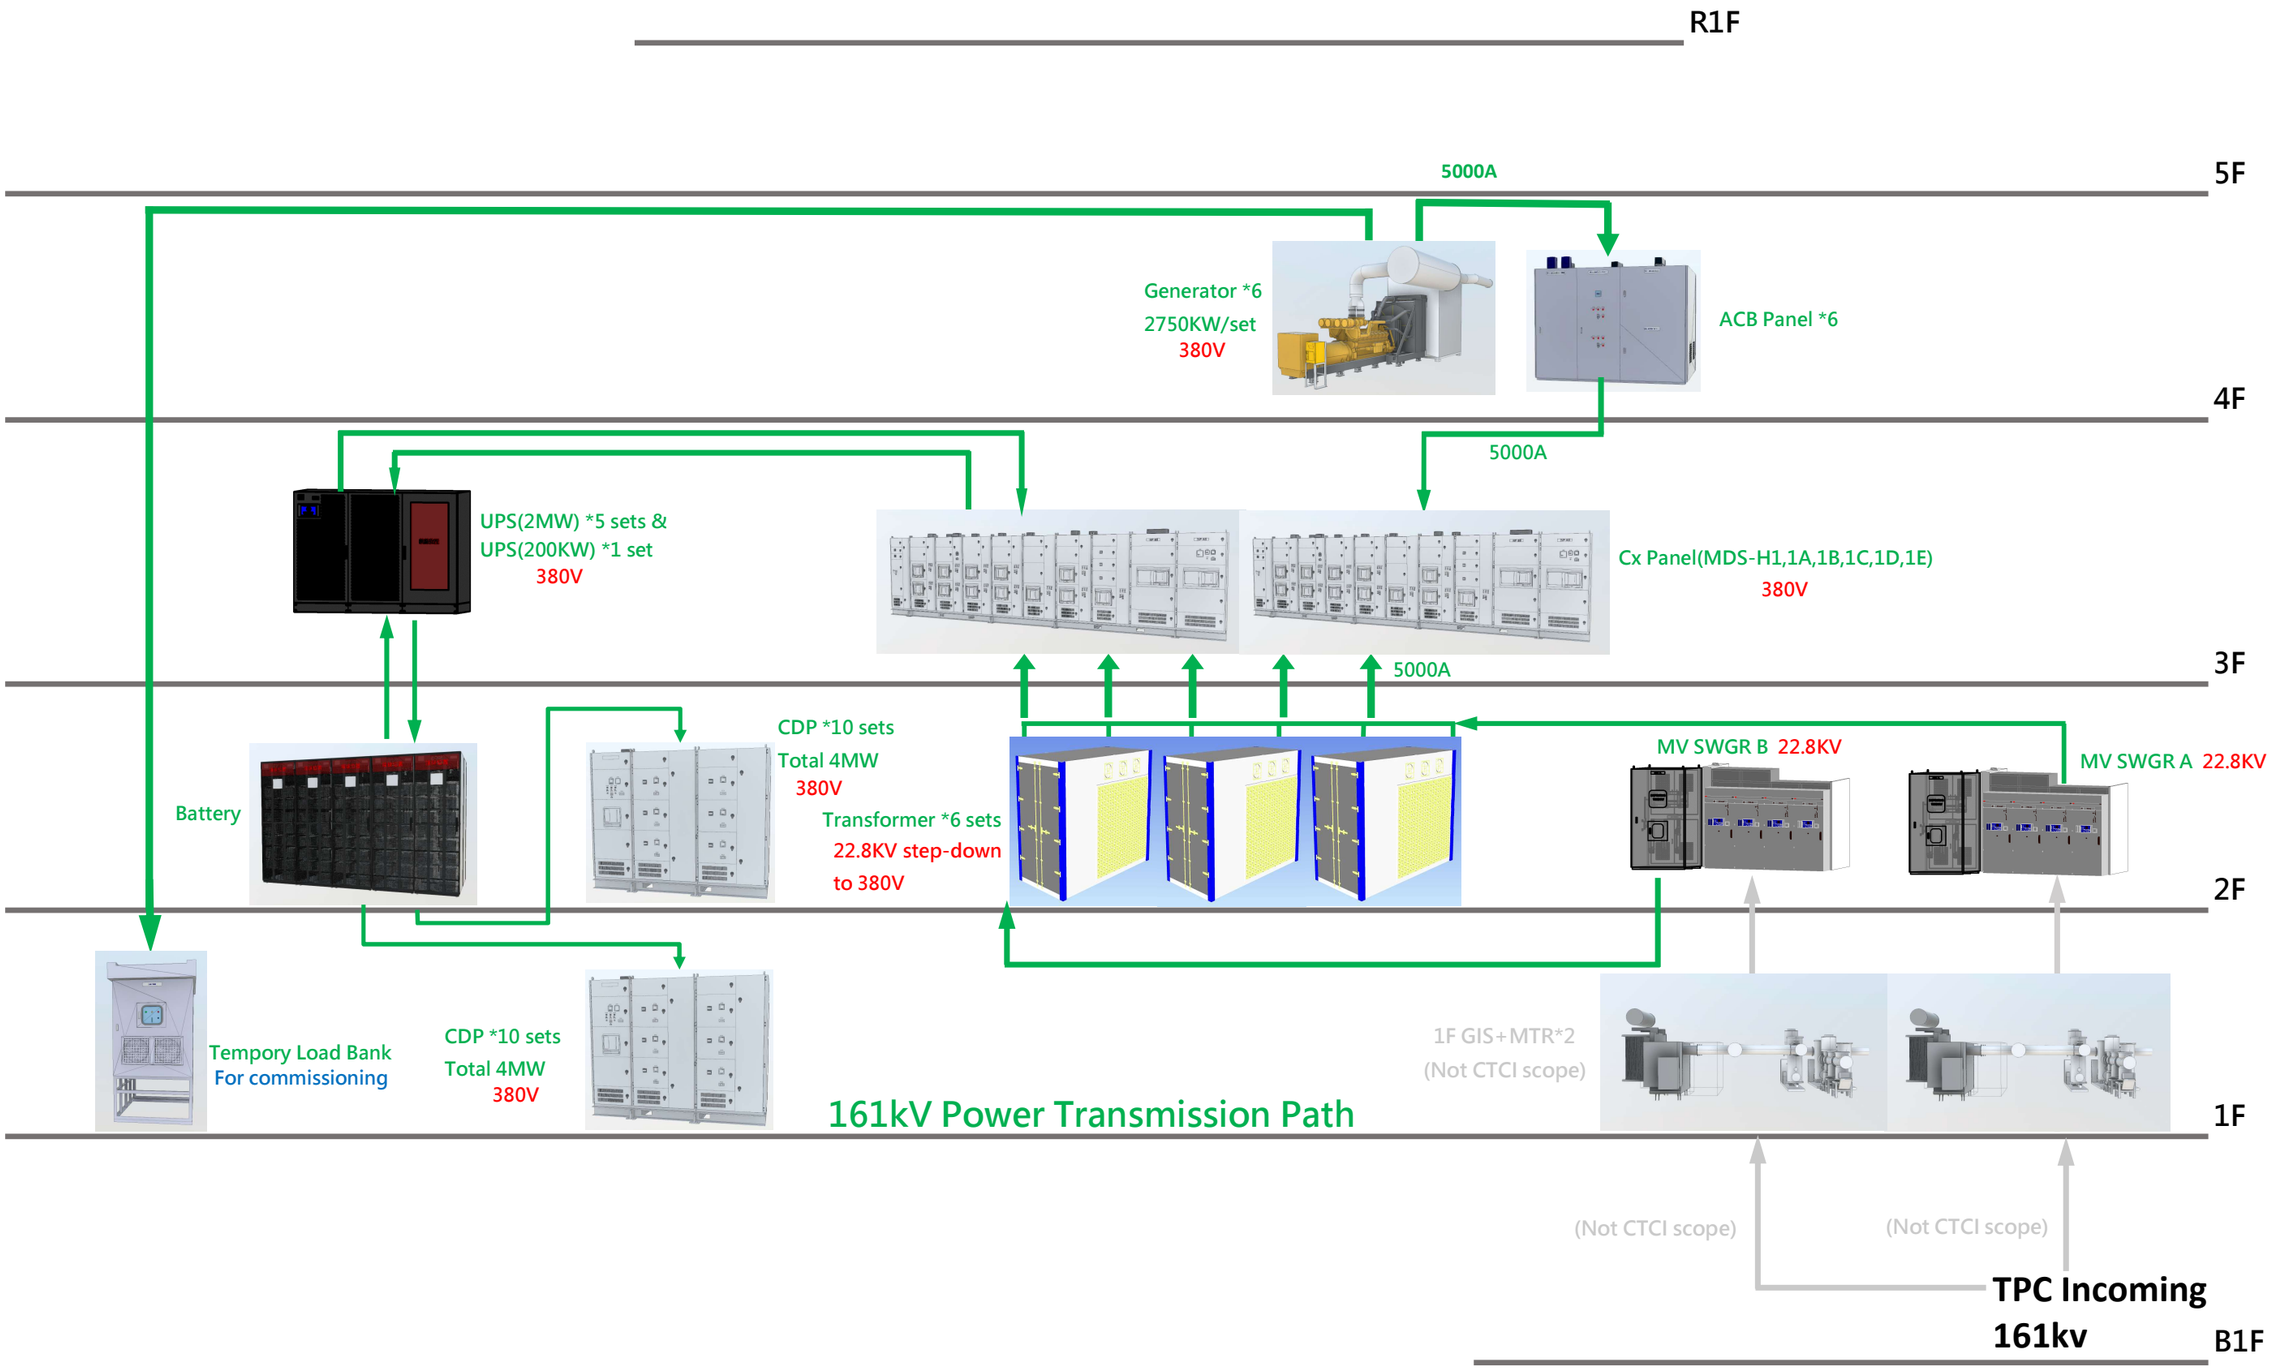
R1F
5F
5000A
Generator *6
2750KW/set
380V
ACB Panel *6
4F
5000A
UPS(2MW) *5 sets &
UPS(200KW) *1 set
380V
Cx Panel(MDS-H1,1A,1B,1C,1D,1E)
380V
3F
5000A
CDP *10 sets
Total 4MW
380V
Battery
Transformer *6 sets
22.8KV step-down
to 380V
MV SWGR B 22.8KV
MV SWGR A 22.8KV
2F
Tempory Load Bank
For commissioning
CDP *10 sets
Total 4MW
380V
1F GIS+MTR*2
(Not CTCI scope)
161kV Power Transmission Path
1F
(Not CTCI scope)
(Not CTCI scope)
TPC Incoming
161kv
B1F