CONFIDENTIALITY NOTICE: THE CONTENT OF THIS DOCUMENT IS SENSITIVE INFORMATION MADE AND OWNED BY MICRON CORPORATION AND IS PROTECTED BY COPYRIGHT LAWS AND RELEVANT LAWS/REGULATIONS. ONLY EMPLOYEES OF MICRON ARE ALLOWED TO ACCESS AND USE THIS SENSITIVE INFORMATION WITHIN THE WORK SCOPE UNDER THE SPECIFIC AND RESPECTIVE DUTIES AND OBLIGATIONS REQUIRED BY AGREEMENT WHICH IS NOT ALLOWED TO COPY, REPRODUCE, DISTRIBUTE PUBLICLY OR DISCLOSE IN WHOLE OR IN PART TO ANY OTHER PARTY WITHOUT CTCI'S PRIOR AND WRITTEN CONSENT.

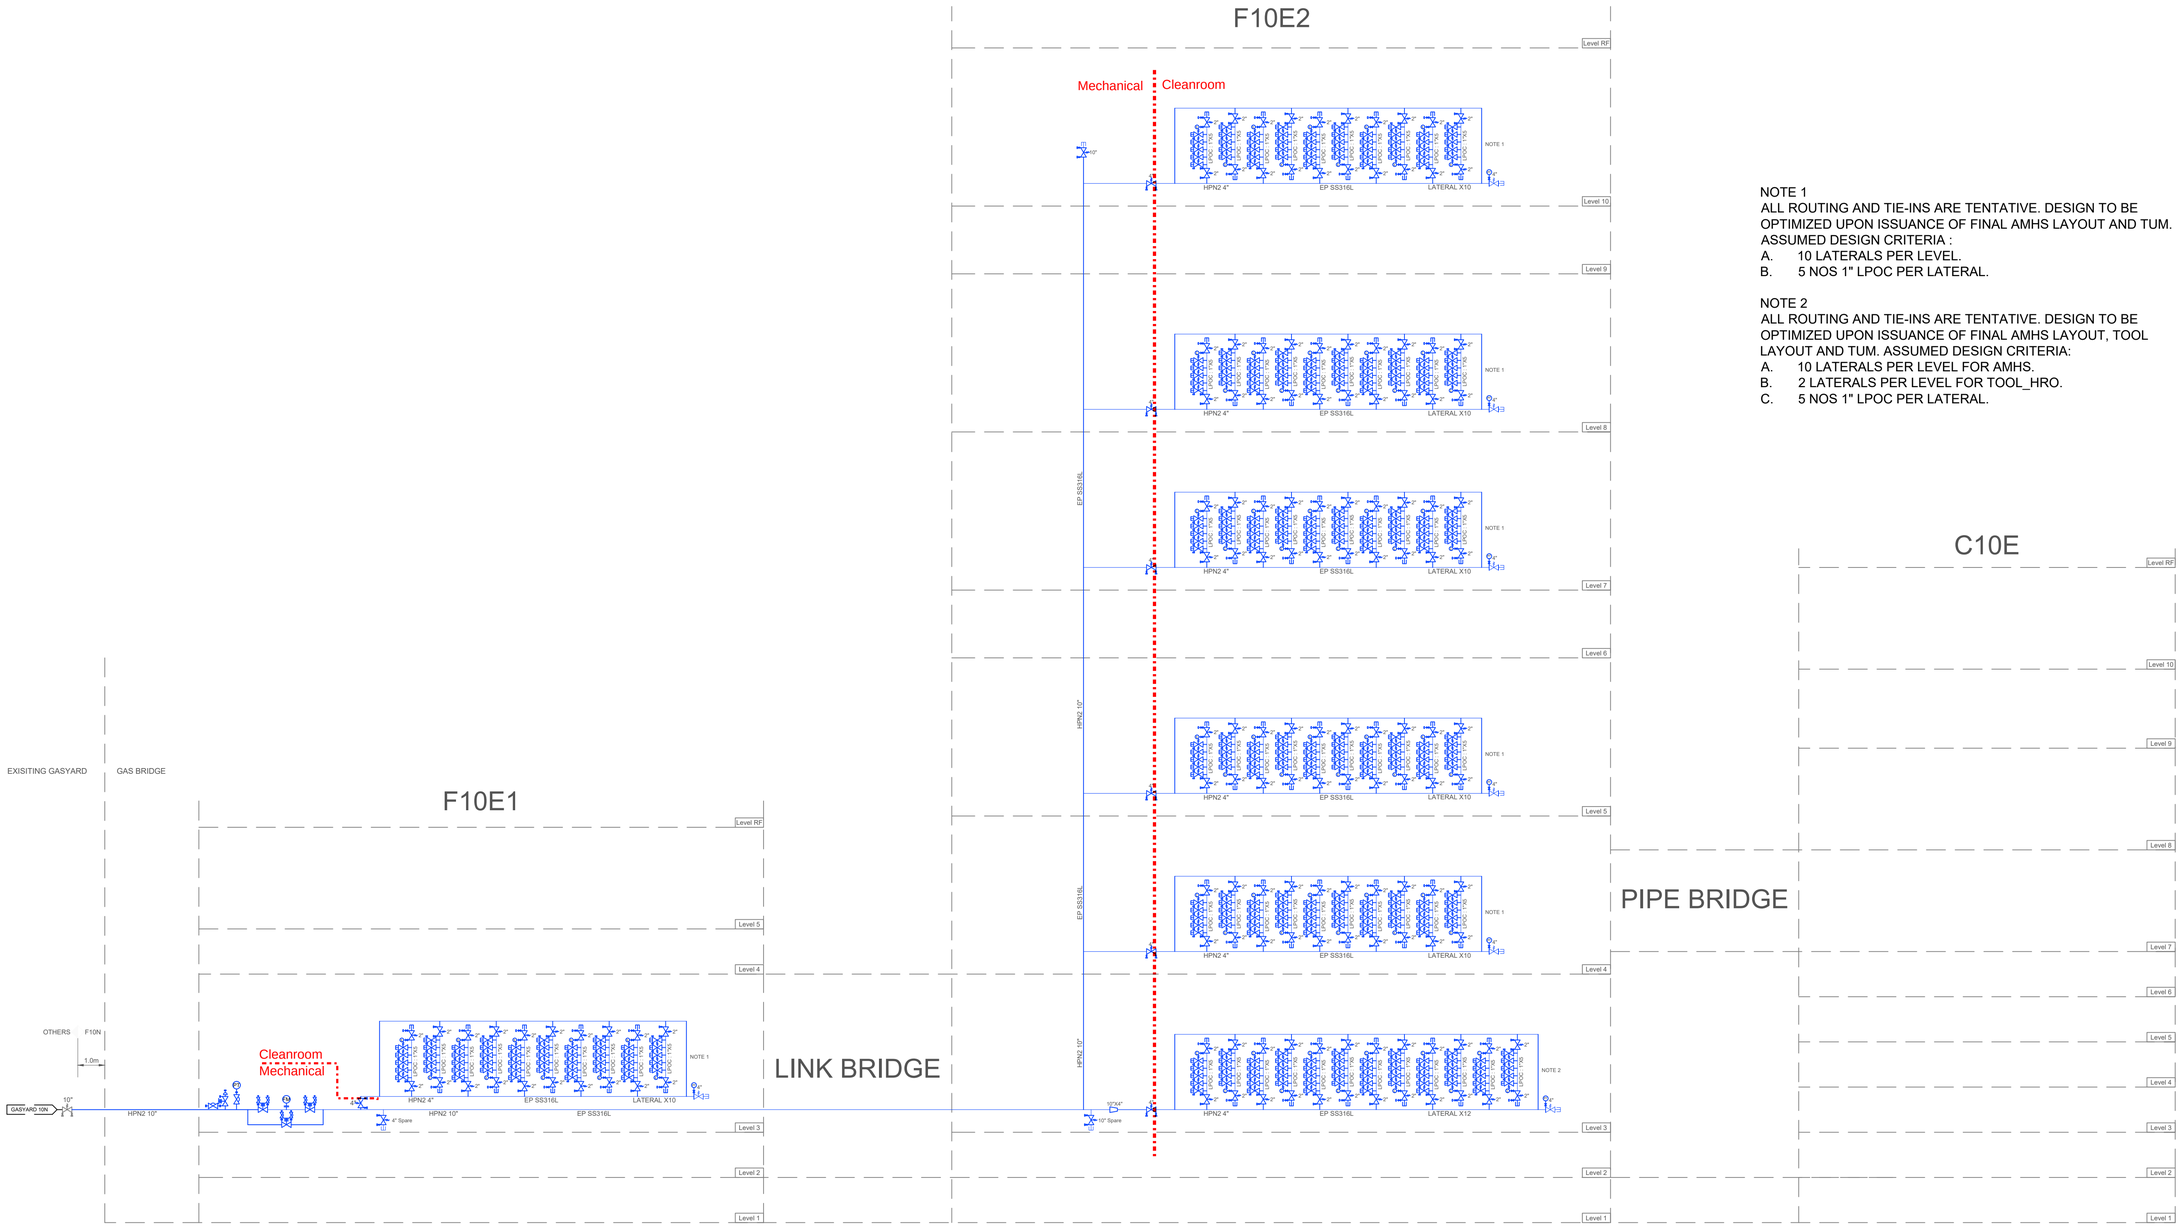

NOTE 1
ALL ROUTING AND TIE-INS ARE TENTATIVE. DESIGN TO BE OPTIMIZED UPON ISSUANCE OF FINAL AMHS LAYOUT AND TUM. ASSUMED DESIGN CRITERIA :
A. 10 LATERALS PER LEVEL.
B. 5 NOS 1" LPOC PER LATERAL.

NOTE 2
ALL ROUTING AND TIE-INS ARE TENTATIVE. DESIGN TO BE OPTIMIZED UPON ISSUANCE OF FINAL AMHS LAYOUT, TOOL LAYOUT AND TUM. ASSUMED DESIGN CRITERIA:
A. 10 LATERALS PER LEVEL FOR AMHS.
B. 2 LATERALS PER LEVEL FOR TOOL_HRO.
C. 5 NOS 1" LPOC PER LATERAL.

F10E Site Elevation
Bulk Gas System Flow Diagram - HPN2

OWNER / DEVELOPER
micron™

ARCHITECTURAL CONSULTANT

CIVIL & STRUCTURAL CONSULTANT

MECHANICAL & ELECTRICAL CONSULTANT

DESIGN MANAGER
CTCI Singapore Pte. Ltd.

PROJECT ADDRESS
North Coast Drive, Singapore

KEY PLAN

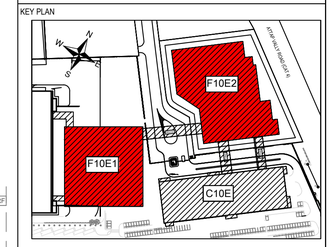

Secret
R3
Level

FOR REVIEW

REV	DATE	DESCRIPTION	ISSUED BY
D	13-Mar-26	ISSUED FOR DESIGN REVIEW 2-1	Robert
C	26-Feb-26	ISSUED FOR DESIGN REVIEW 2	Robert
B	12-Feb-26	ISSUED FOR DESIGN REVIEW 1-1	Robert
A	26-Jan-26	ISSUED FOR DESIGN REVIEW 1	Robert

Revisions

PROJECT TITLE
Micron F10E Probe Project

PROJECT PHASE
A&E

DRAWING TITLE
MICRON NEW PROBE OVERALL
Process Flow Diagram
HPN2 Distribution

DESIGNED : Robert	DRAWN : Johnson	CHECKED : Robert
DATE : 26/02/26	JOB NO. :	SCALE :

Micron DRAWING NO.	F21B-F10E-PFD-S0-00-P-101	REV
CTCI DRAWING NO.		D
Reference Model		

CTCI	SHEET: 1 OF 1	SIZE A1

CONFIDENTIALITY NOTICE: THE CONTENT OF THIS DOCUMENT IS SENSITIVE INFORMATION MADE AND OWNED BY MICRON CORPORATION AND IS PROTECTED BY COPYRIGHT LAWS AND RELEVANT LAWS/REGULATIONS. ONLY EMPLOYEES OF MICRON ARE ALLOWED TO ACCESS AND USE THIS SENSITIVE INFORMATION WITHIN THE WORK SCOPE UNDER THEIR SPECIFIC AND RESPECTIVE DUTIES AND OBLIGATIONS REQUIRED BY AGREEMENT WHICH IS NOT ALLOWED TO COPY, REPRODUCE, DISTRIBUTE PUBLICLY OR DISCLOSE IN WHOLE OR IN PART TO ANY OTHER PARTY WITHOUT CTCI'S PRIOR AND WRITTEN CONSENT.

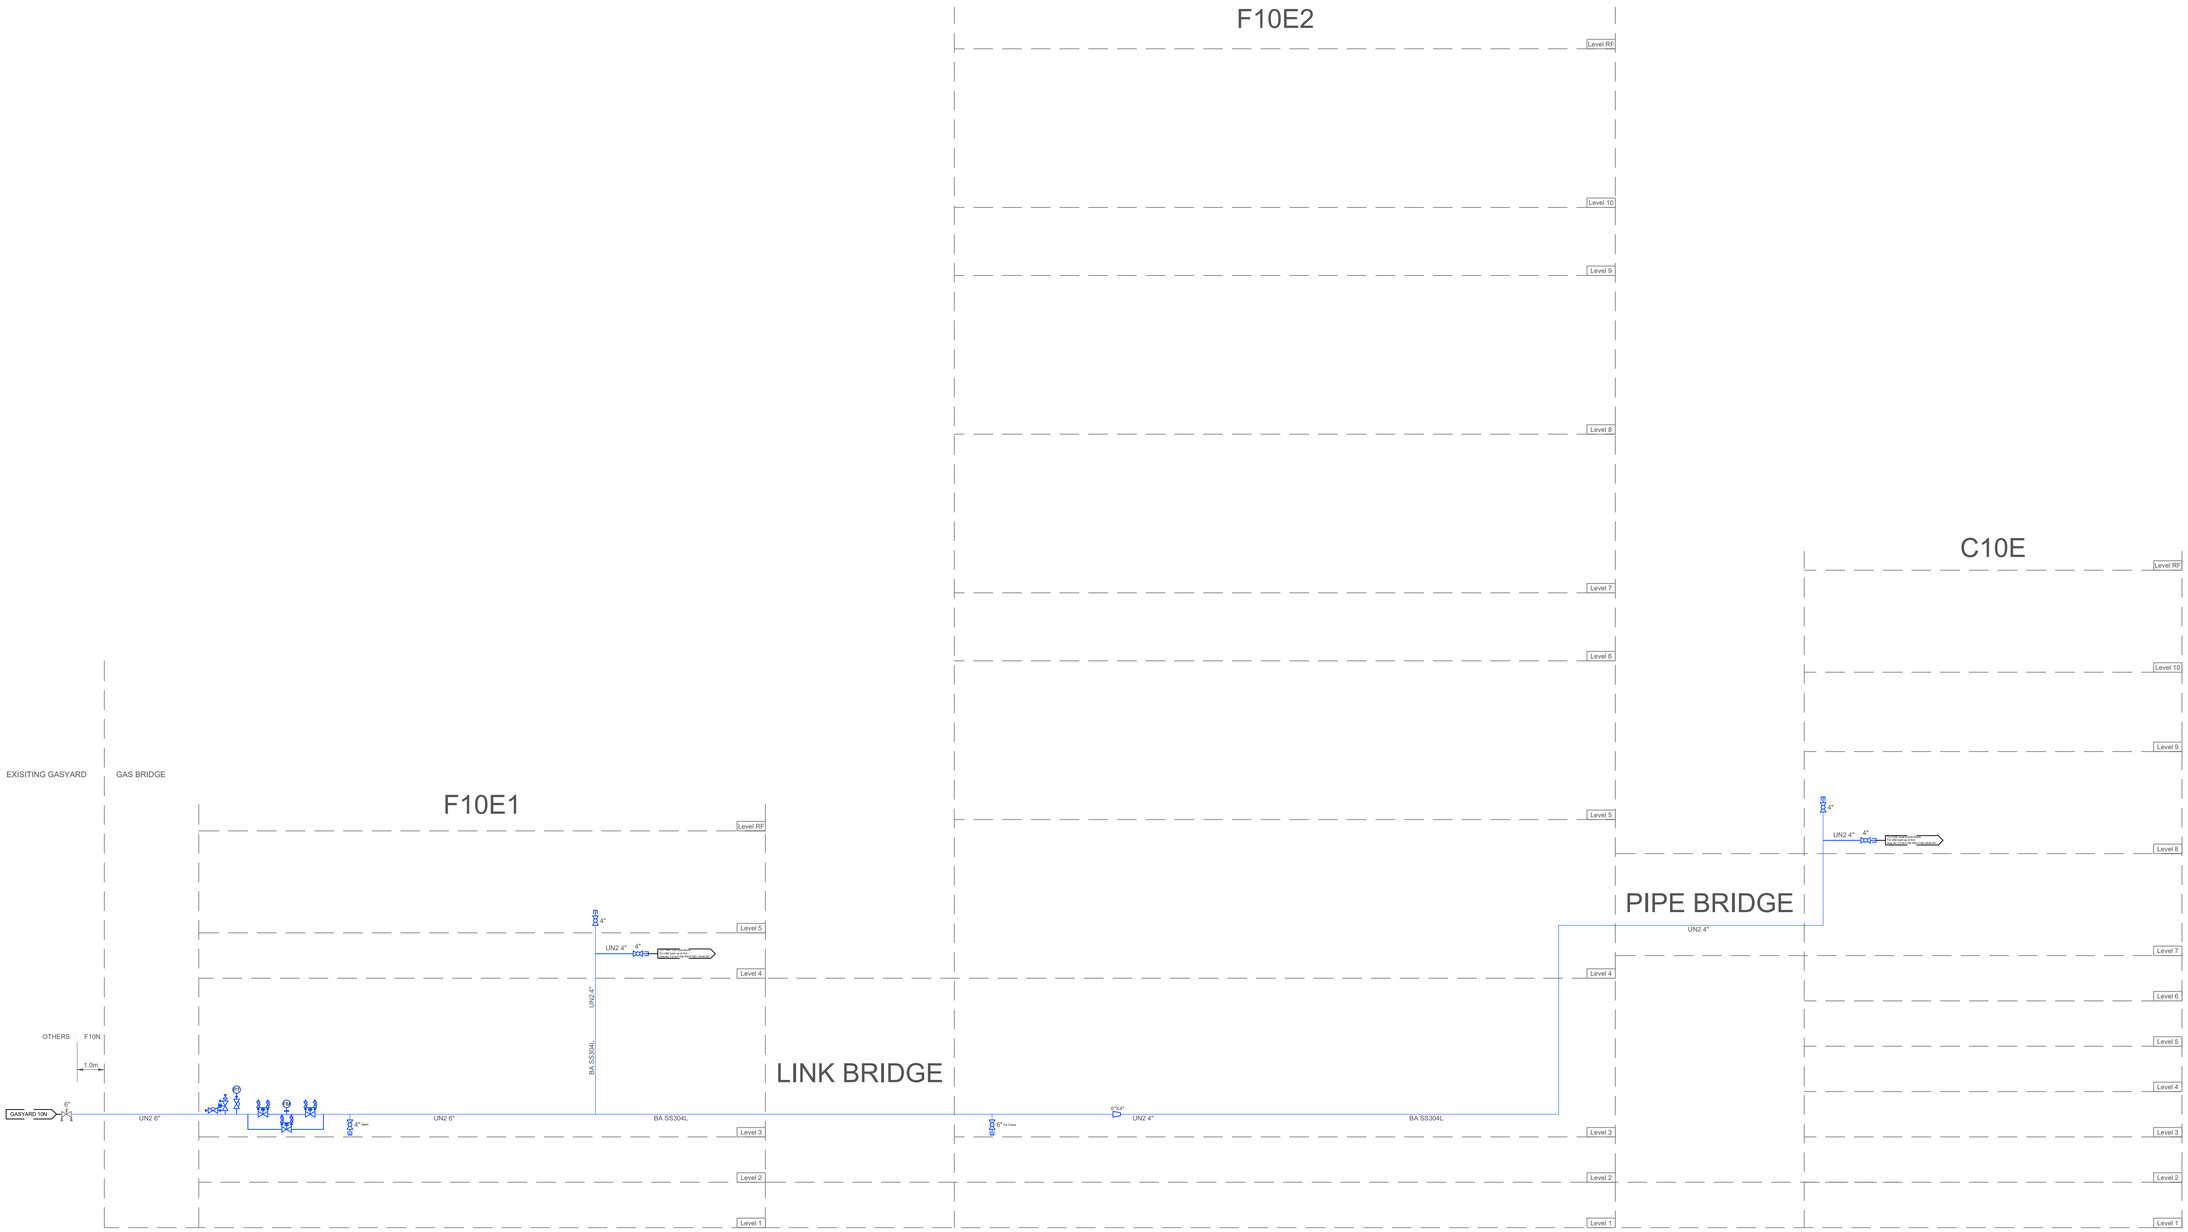

F10E Site Elevation

Bulk Gas System Flow Diagram - UN2

OWNER / DEVELOPER

micron™

ARCHITECTURAL CONSULTANT

CIVIL & STRUCTURAL CONSULTANT

MECHANICAL & ELECTRICAL CONSULTANT

DESIGN MANAGER

CTCI Singapore Pte. Ltd.

PROJECT ADDRESS

North Coast Drive, Singapore

KEY PLAN

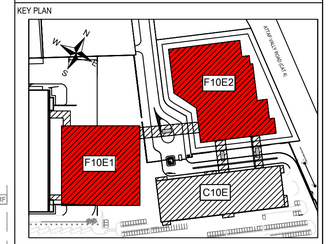

Secret
R3
Level

FOR REVIEW

REV	DATE	DESCRIPTION	ISSUED BY
D	13-Mar-26	ISSUED FOR DESIGN REVIEW 2-1	Robert
C	26-Feb-26	ISSUED FOR DESIGN REVIEW 2	Robert
B	12-Feb-26	ISSUED FOR DESIGN REVIEW 1-1	Robert
A	26-Jan-26	ISSUED FOR DESIGN REVIEW 1	Robert

Revisions

PROJECT TITLE

Micron F10E Probe Project

PROJECT PHASE

A&E

DRAWING TITLE

MICRON NEW PROBE OVERALL
Process Flow Diagram
UN2 Distribution

DESIGNED : Robert	DRAWN : Johnson	CHECKED : Robert
DATE : 26/02/26	JOB NO. :	SCALE :

Micron DRAWING NO.	F21B-F10E-PFD-S0-00-P-102	REV D
CTCI DRAWING NO.		
Reference Model		

CTCI	SHEET: 1 OF 1	SIZE A1

CONFIDENTIALITY NOTICE: THE CONTENT OF THIS DOCUMENT IS SENSITIVE INFORMATION MADE AND OWNED BY MICRON CORPORATION AND IS PROTECTED BY COPYRIGHT LAWS AND RELEVANT LAWS/REGULATIONS. ONLY EMPLOYEES OF MICRON ARE ALLOWED TO ACCESS AND USE THIS SENSITIVE INFORMATION WITHIN THE WORK SCOPE UNDER THEIR SPECIFIC AND RESPECTIVE DUTIES AND OBLIGATIONS REQUIRED BY AGREEMENT WHICH IS NOT ALLOWED TO COPY, REPRODUCE, DISTRIBUTE PUBLICLY OR DISCLOSE IN WHOLE OR IN PART TO ANY OTHER PARTY WITHOUT CTCI'S PRIOR AND WRITTEN CONSENT.

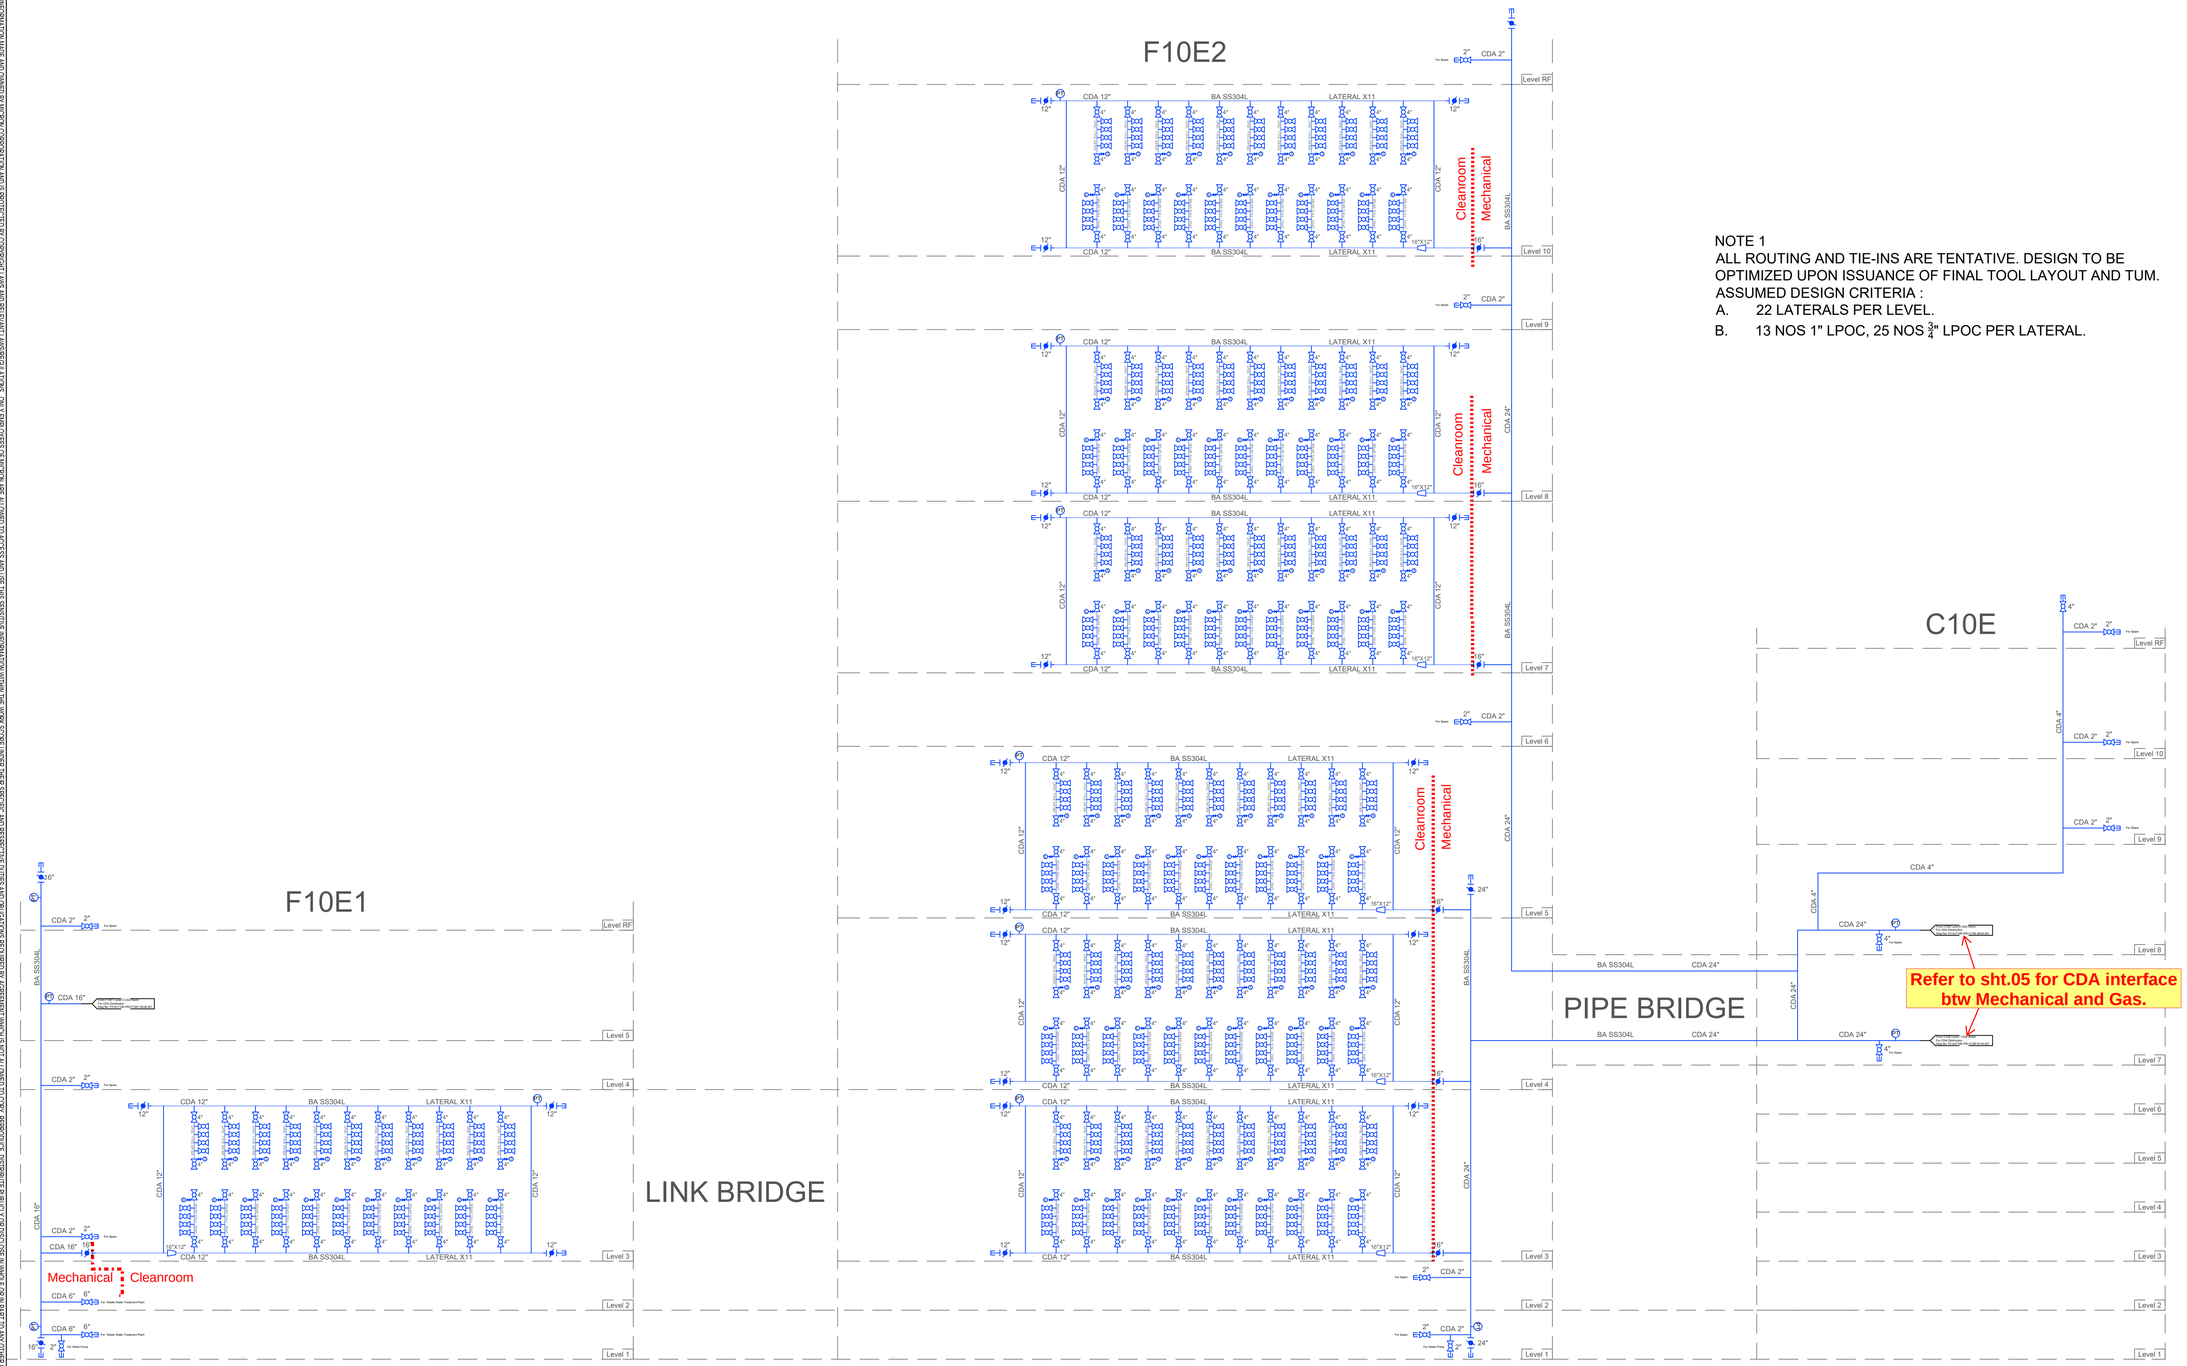

NOTE 1
ALL ROUTING AND TIE-INS ARE TENTATIVE. DESIGN TO BE OPTIMIZED UPON ISSUANCE OF FINAL TOOL LAYOUT AND TUM.
ASSUMED DESIGN CRITERIA :

A. 22 LATERALS PER LEVEL.

B. 13 NOS 1" LPOC, 25 NOS $\frac{3}{4}$" LPOC PER LATERAL.

F10E Site Elevation

Bulk Gas System Flow Diagram - CDA

OWNER / DEVELOPER

micron™

ARCHITECTURAL CONSULTANT

CIVIL & STRUCTURAL CONSULTANT

MECHANICAL & ELECTRICAL CONSULTANT

DESIGN MANAGER

CTCI Singapore Pte. Ltd.

PROJECT ADDRESS

North Coast Drive, Singapore

KEY PLAN

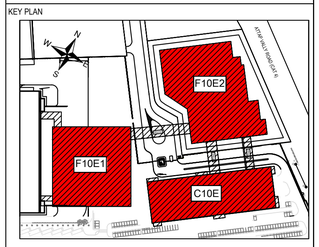

Secret
R3
Level

FOR REVIEW

REV	DATE	DESCRIPTION	ISSUED BY
D	13-Mar-26	ISSUED FOR DESIGN REVIEW 2-1	Robert
C	26-Feb-26	ISSUED FOR DESIGN REVIEW 2	Robert
B	12-Feb-26	ISSUED FOR DESIGN REVIEW 1-1	Robert
A	26-Jan-26	ISSUED FOR DESIGN REVIEW 1	Robert

Revisions

PROJECT TITLE

Micron F10E Probe Project

PROJECT PHASE

A&E

DRAWING TITLE

MICRON NEW PROBE OVERALL
Process Flow Diagram
CDA Distribution

DESIGNED : Robert	DRAWN : Johnson	CHECKED : Robert
DATE : 26/02/26	JOB NO. :	SCALE :

Micron DRAWING NO.	F21B-F10E-PFD-S0-00-P-103	REV D
CTCI DRAWING NO.		
Reference Model		
CTCI	SHEET: 1 OF 1	SIZE A1

CONFIDENTIALITY NOTICE: THE CONTENT OF THIS DOCUMENT IS SENSITIVE INFORMATION MADE AND OWNED BY MICRON CORPORATION AND IS PROTECTED BY COPYRIGHT LAWS AND RELEVANT LAWS/REGULATIONS. ONLY EMPLOYEES OF MICRON ARE ALLOWED TO ACCESS AND USE THIS SENSITIVE INFORMATION WITHIN THE WORK SCOPE UNDER THE SPECIFIC AND RESPECTIVE ENTIES AND OBLIGATIONS REQUIRED BY AGREEMENT WHICH IS NOT ALLOWED TO COPY, REPRODUCE, DISTRIBUTE PUBLICLY OR DISCLOSE IN WHOLE OR IN PART TO ANY OTHER PARTY WITHOUT CTCI'S PRIOR AND WRITTEN CONSENT.

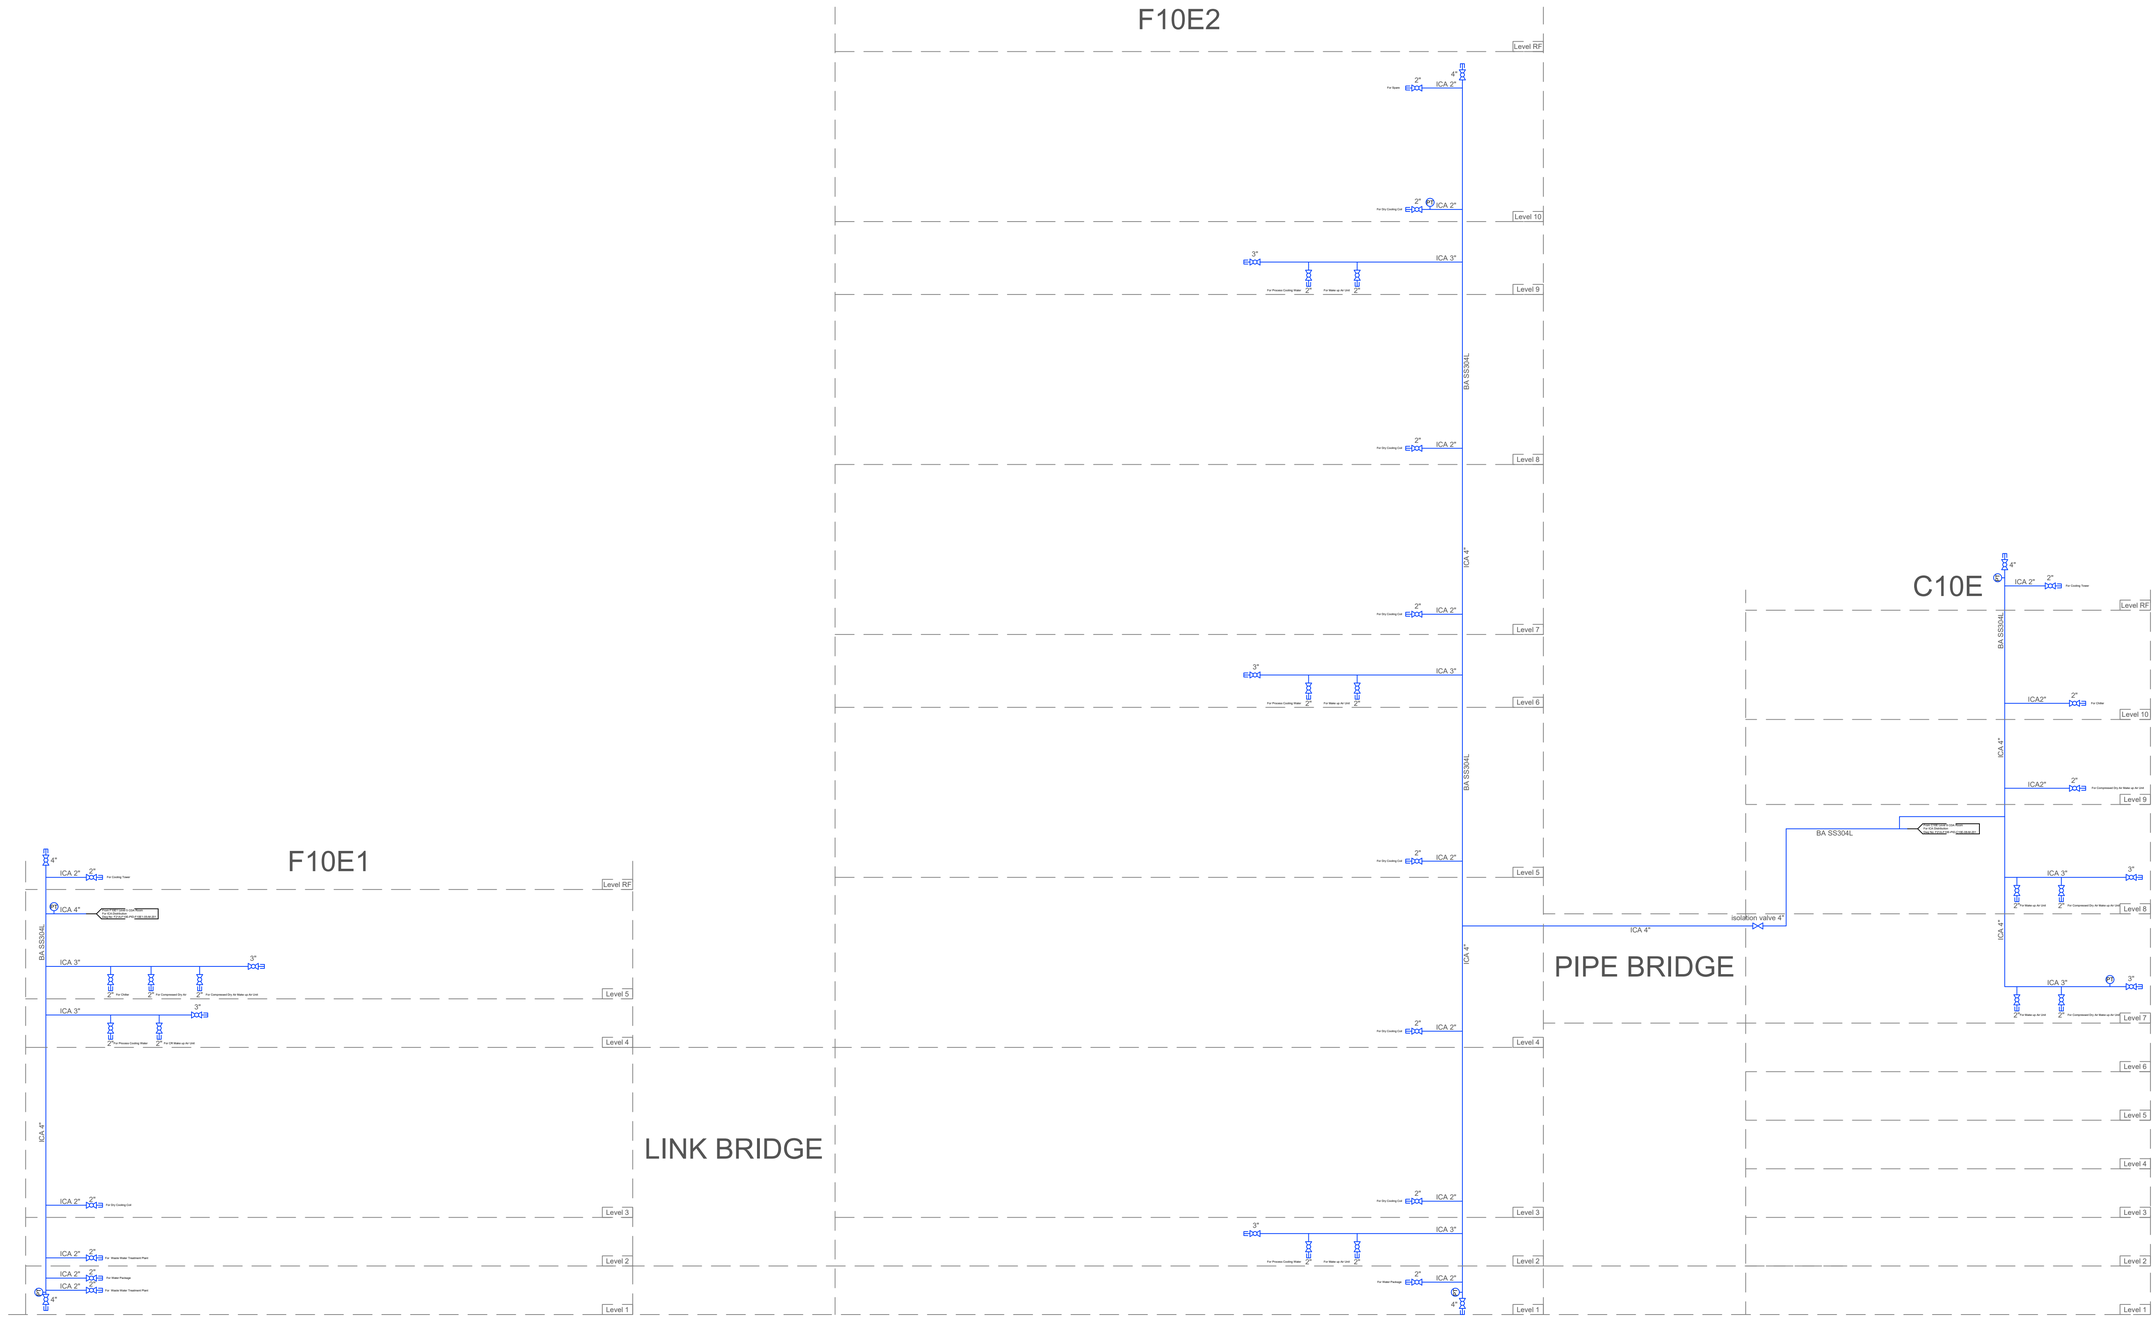

F10E Site Elevation

Bulk Gas System Flow Diagram - ICA

OWNER / DEVELOPER

micron™

ARCHITECTURAL CONSULTANT

CIVIL & STRUCTURAL CONSULTANT

MECHANICAL & ELECTRICAL CONSULTANT

DESIGN MANAGER

CTCI Singapore Pte. Ltd.

PROJECT ADDRESS

North Coast Drive, Singapore

KEY PLAN

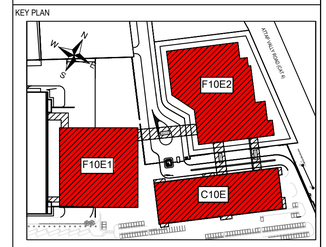

Secret
R3
Level

FOR REVIEW

REV	DATE	DESCRIPTION	ISSUED BY
D	13-Mar-26	ISSUED FOR DESIGN REVIEW 2-1	Robert
C	26-Feb-26	ISSUED FOR DESIGN REVIEW 2	Robert
B	12-Feb-26	ISSUED FOR DESIGN REVIEW 1-1	Robert
A	26-Jan-26	ISSUED FOR DESIGN REVIEW 1	Robert

Revisions

PROJECT TITLE

Micron F10E Probe Project

PROJECT PHASE

A&E

DRAWING TITLE

MICRON NEW PROBE OVERALL
Process Flow Diagram
ICA Distribution

DESIGNED : Robert	DRAWN : Johnson	CHECKED : Robert
DATE : 26/02/26	JOB NO. :	SCALE :

Micron DRAWING NO.	F21B-F10E-PFD-S0-00-P-104	REV D
CTCI DRAWING NO.		
Reference Model		
CTCI	SHEET: 1 OF 1	SIZE A1
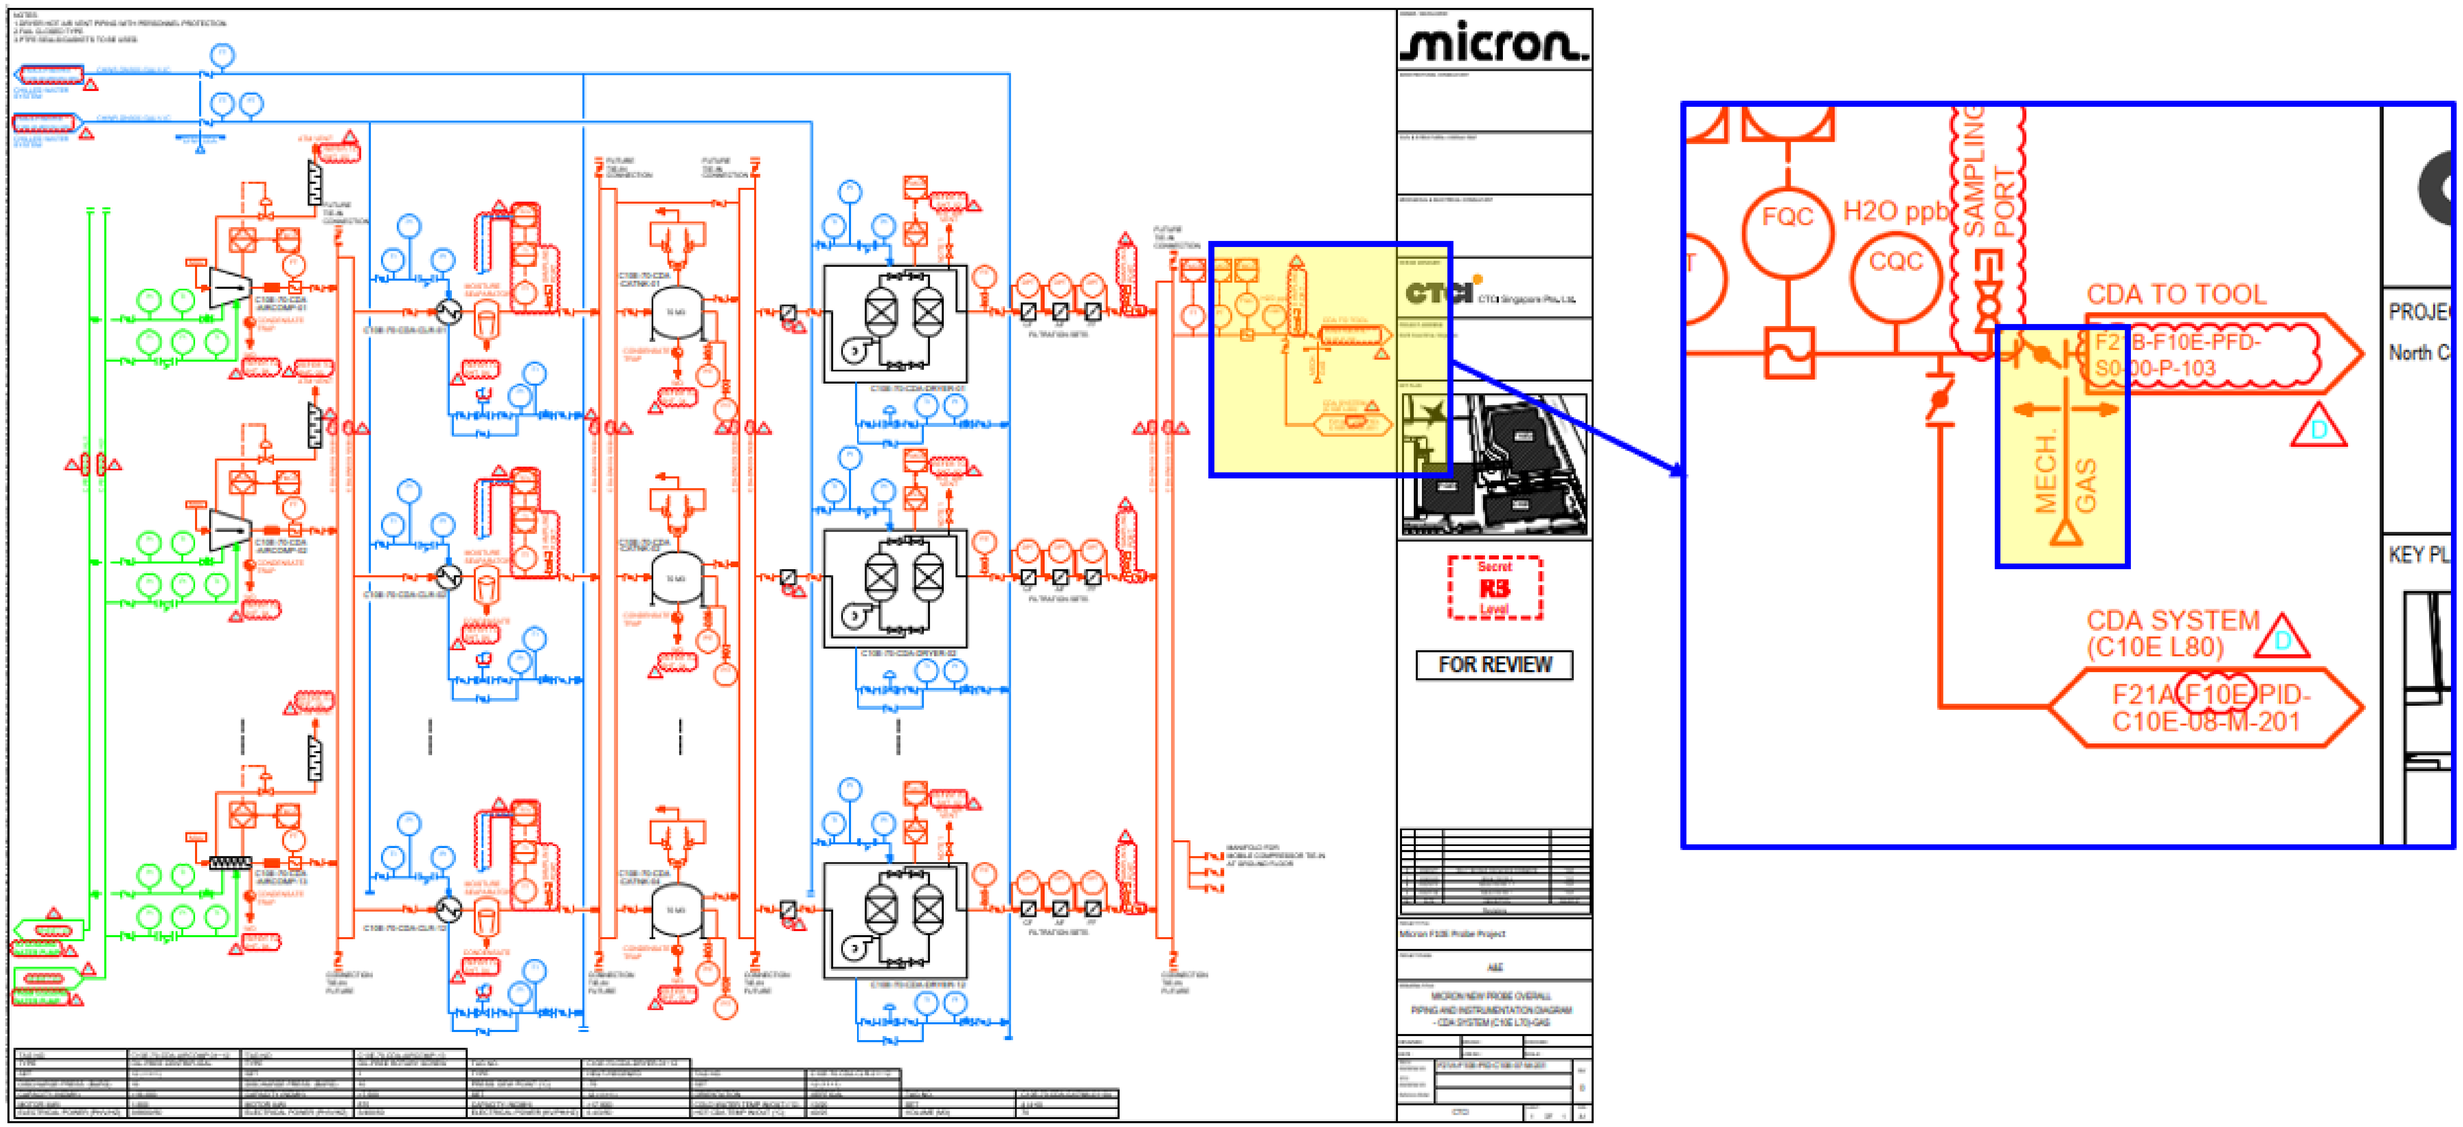
CDA Mechanical & Gas Interface